P68 underway: midship section at heel (schematic, not a rendering)

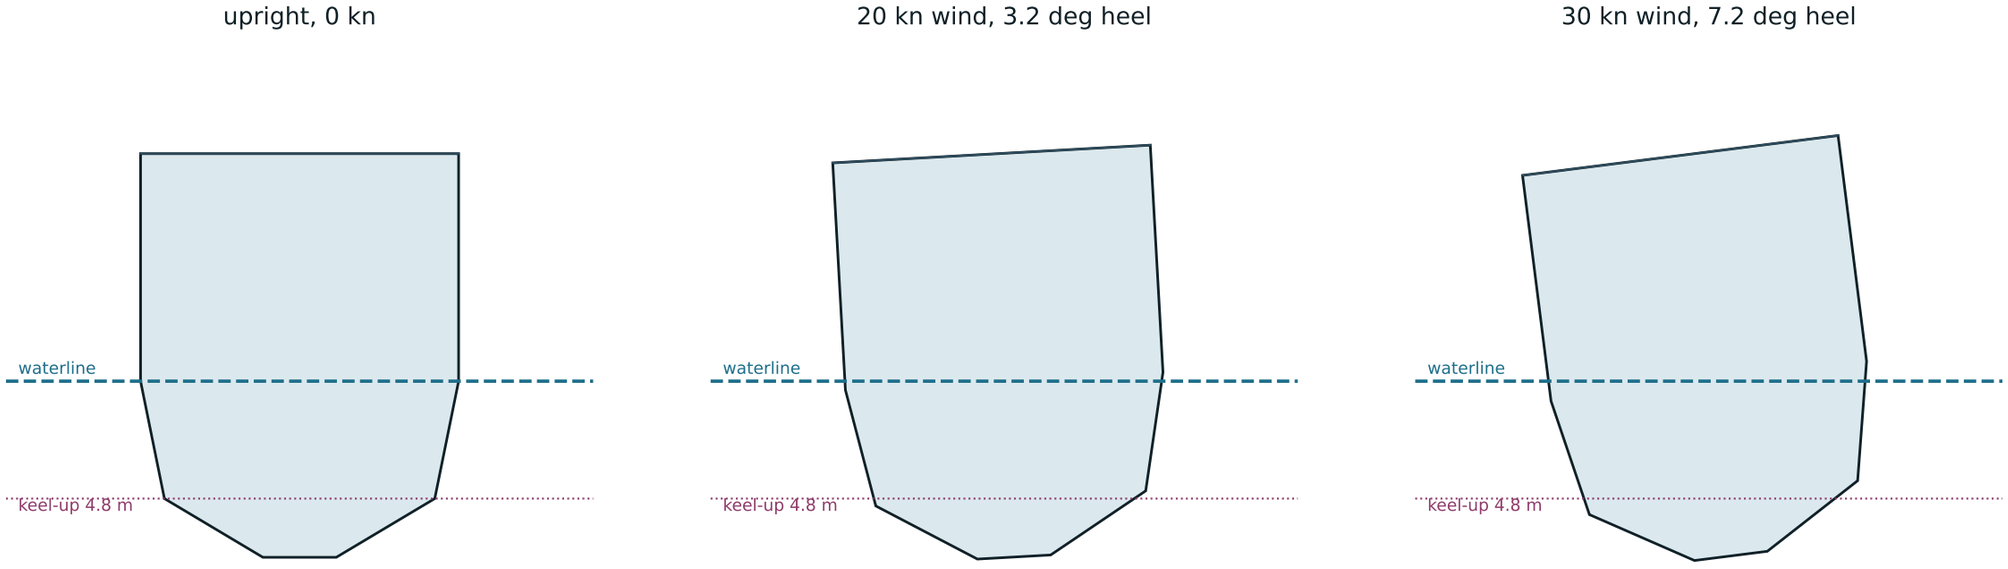

Section at 120 m LOA, 20.0 m beam. Heel from the placeholder sail (600 m², Cf 0.7, h 30 m) at GM 1.0 m. The waterline is shown level; the hull heels about it.

CONCEPT - NOT FOR CONSTRUCTION. Open design release, Class 1: concept and educational release. Licence to be confirmed.