CIRCULATION AND EGRESS (concept): lifts, stairs, medical bay, tender storage, exits

Route A: medical bay to lift B, then Main to the stern exit (accessible route).

Route B: medical bay to the Tween-Tank stair, then Tank to the stern exit. Tender route: storage to the exit.

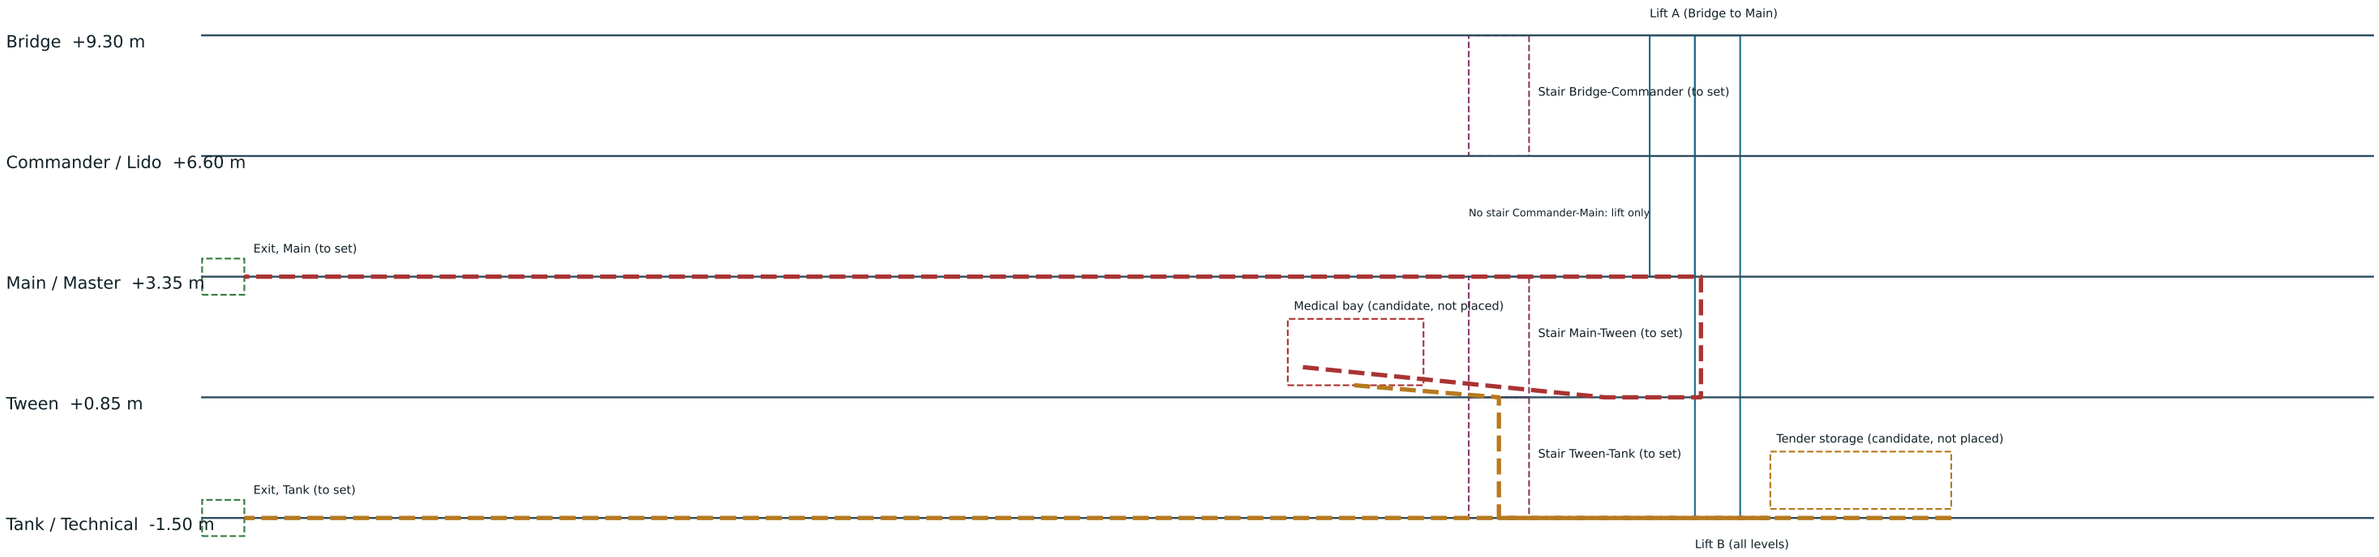

Concept circulation sheet. 120 m LOA. Drawing metres, real size.

Stairs, exits, medical bay and tender storage are NOT placed on the layout: drawn as labelled candidates. Lifts are for accessible movement, not escape. Routes are concept only.

CONCEPT - NOT FOR CONSTRUCTION 10 Oct 2026 SHEET 9

OPEN DESIGN RELEASE - Class 1: concept and educational release. Licence: To be confirmed. The design release policy requires licence ownership to be resolved before any distribution is promised.
Funding: If crowdfunding is used, funds may support design development and a privately owned yacht. Published design data is separate from private ownership. Milestone budgets, release conditions and refund terms will be published before any campaign.